


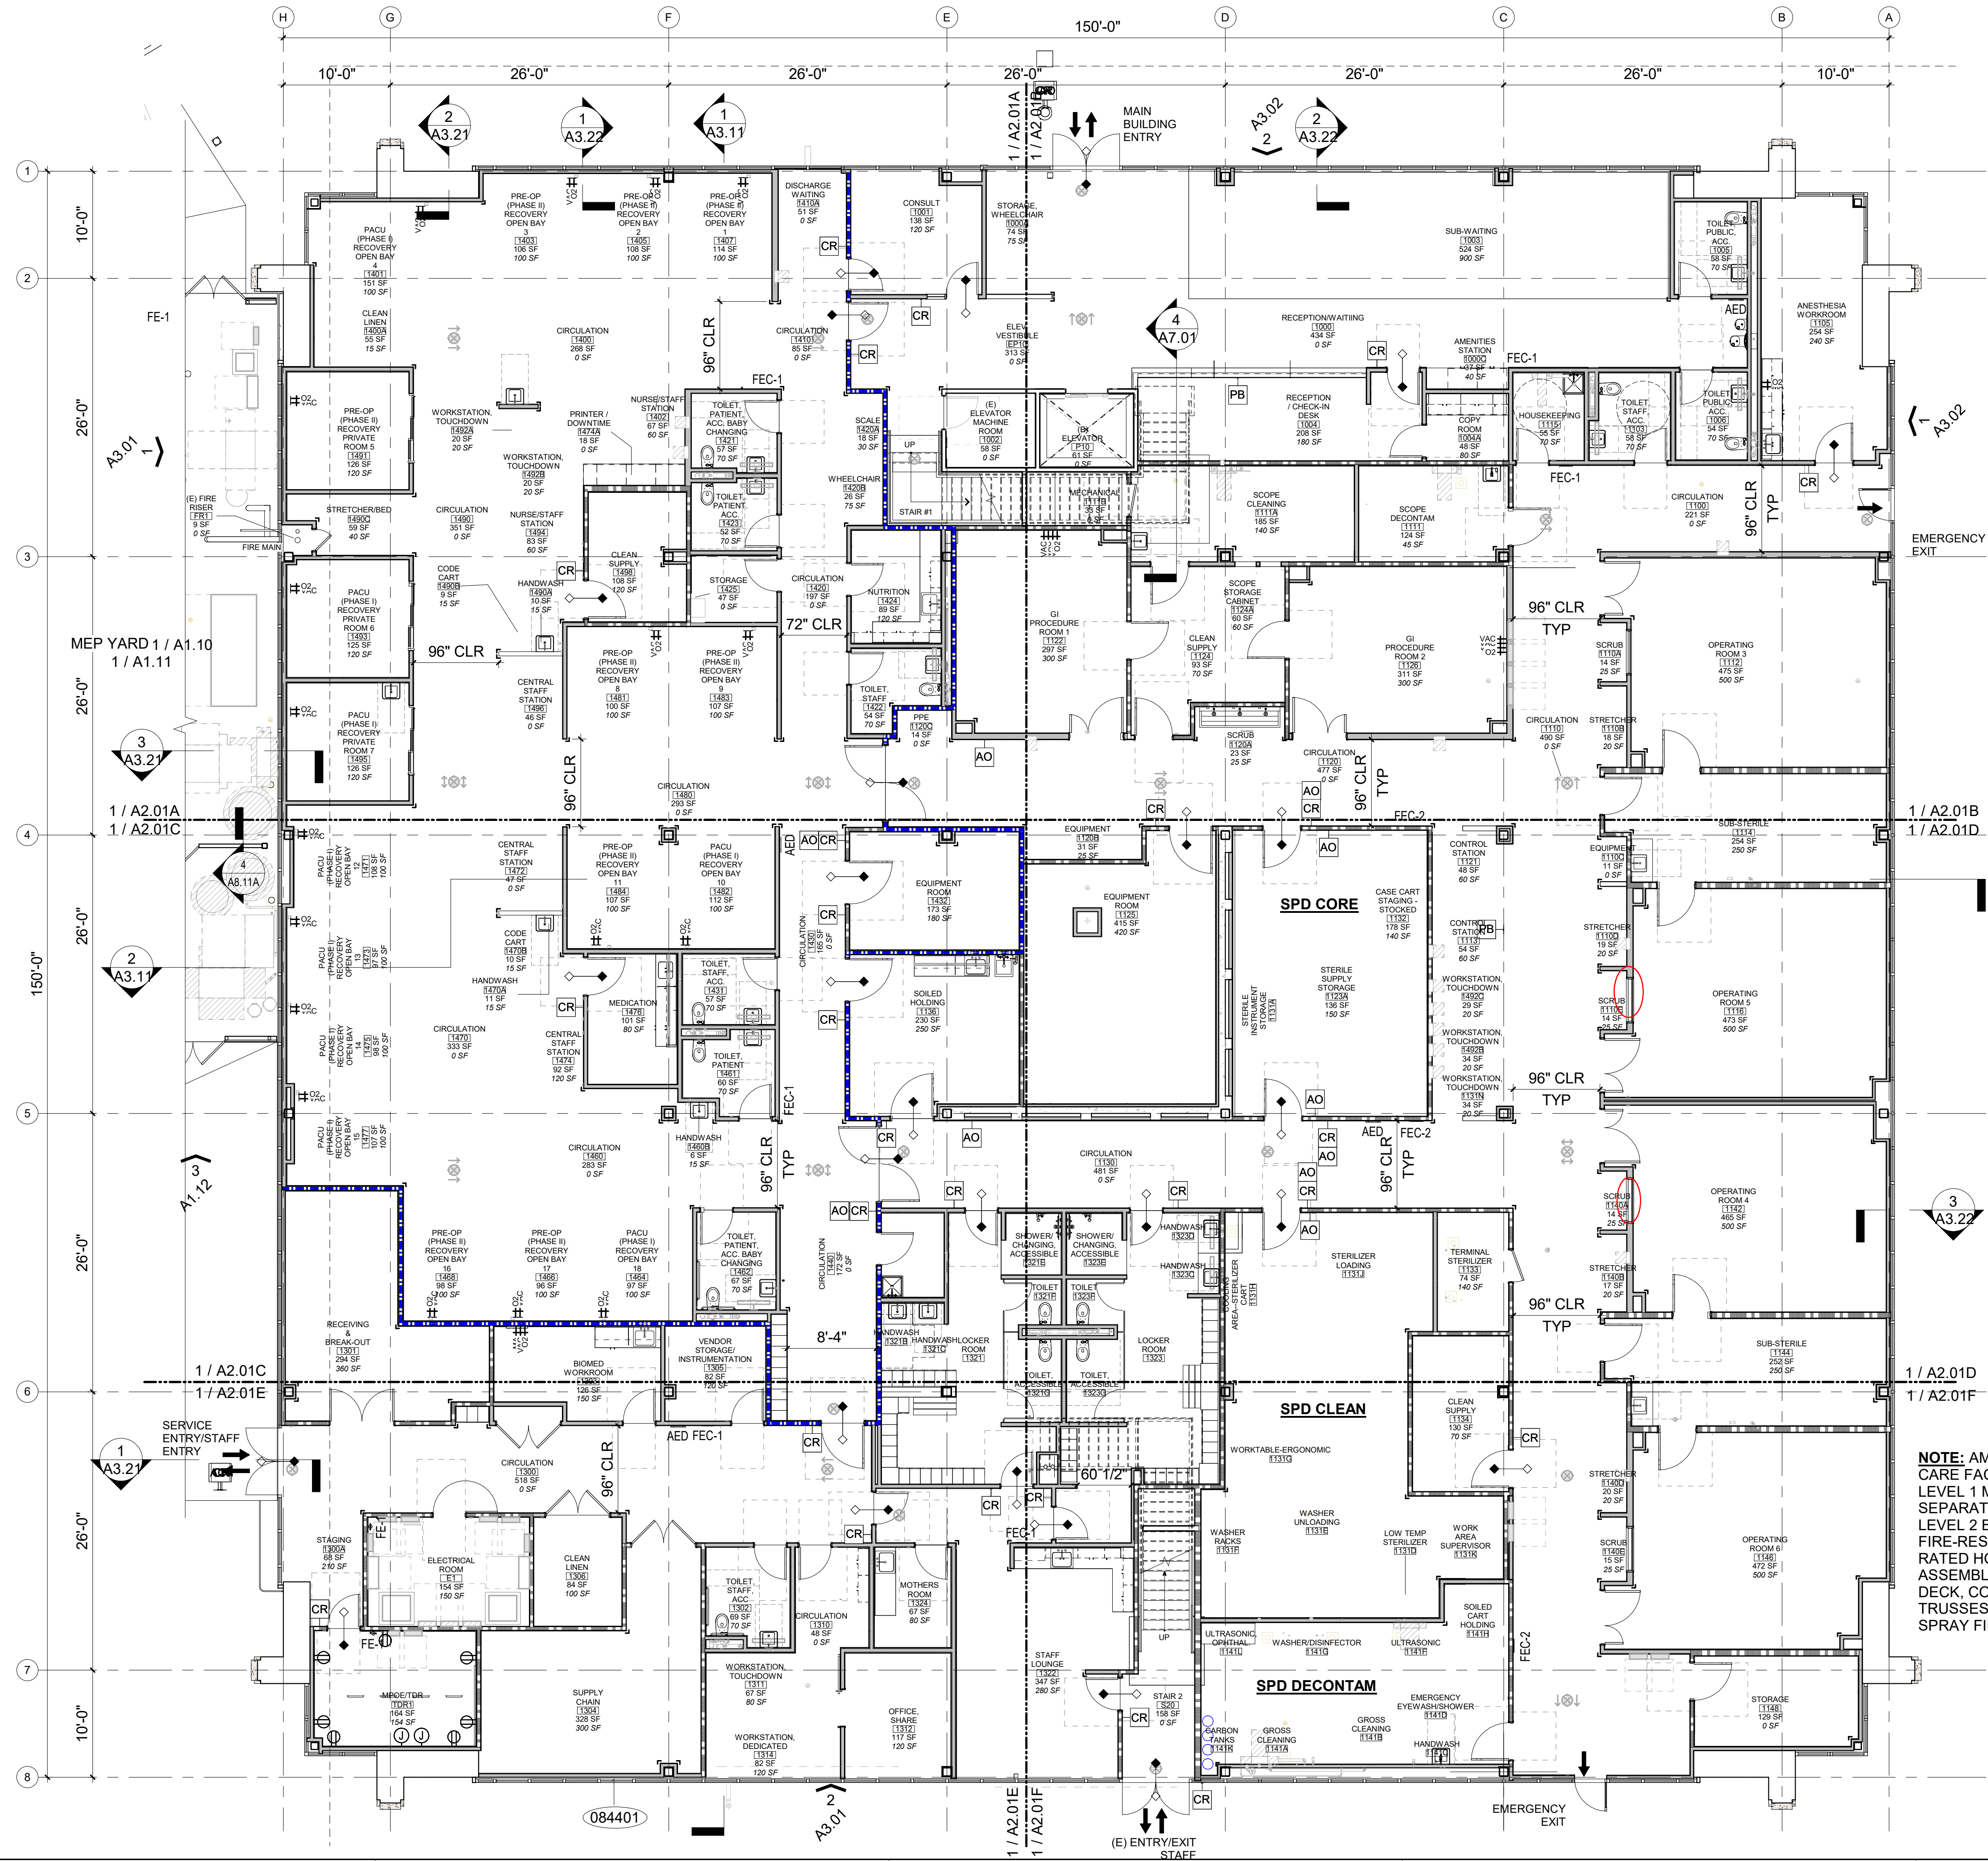

GENERAL PLAN NOTES

- CONTRACTOR TO NOTIFY ARCHITECT OF ANY DISCREPANCY BETWEEN (E) CONDITIONS AND DRAWINGS PRIOR TO PROCEEDING WITH CONSTRUCTION WORK.
- SEE STRUCTURAL, TECHNOLOGY, MEP DWGS FOR EXTENT OF WORK.
- SEE SHEET A1 SERIES, CIVIL & LANDSCAPE DWGS. FOR SITE PLAN AND THE EXTENT OF WORK AROUND THE BUILDING
- SEE SIGNAGE SHEET SERIES SG FOR SIGNAGE INFORMATION
- CONTRACTOR TO COORDINATE FIRE SPRINKLER AND FIRE ALARM SYSTEM.
- EMERGENCY OUTLETS AND NURSE CALL SHOWN ON ELEC AND TECH DWGS
- SEE G4.01, G4.02, G4.03, & G4.04 FOR TYP. MOUNTING HTS., PROVIDE BLOCKING FOR ALL WALL MOUNTED ITEMS PER DETAILS
- SEE SHEET A2.31, A2.32, A9.05 FOR FINISHES AND A9.06 FOR TYP. RESTROOM ACCESSORIES. SEE A2.33 FOR FURNITURE
- SEE A4.01 SERIES AND A4.02 FOR RCPS.
- SEE A9.03A-C FOR EQPT. SCHDL AND A9.06 FOR IT EQPT SCHDL
- ALL WALLS 0D3A U.O.N. ON A2.01A-A2.01F

KEYNOTES

#	NOTE
084401	INFILL CURTAIN WALL GLAZING PANEL WHERE (E) DOOR REMOVED. GLAZING TO MATCH (E)

LEGEND

- NEW 1-HOUR RATED FIRE SMOKE BARRIER
- NEW 1-HOUR RATED FIRE BARRIER
- EXISTING PARTITION TO REMAIN
- NEW UNRATED PARTITION
- CUT AND PATCH (E) TPO ROOF



1420 SUTTER ST
SAN FRANCISCO, CA 94109
T 415.391.7918 F 415.391.7309
TEFarch.com



CONSULTANTS:
STRUCTURAL: FORELL/ELSESSER
CIVIL: SANDIS
LANDSCAPE: CREO
LOW VOLTAGE: INTROBA
ACOUSTICAL: SALTER
CODE: JENSEN HUGHES

**SHC Hacienda
Lakes Ambulatory
Surgical Center**


4457 Willow Rd
Pleasanton, CA



Project Number: 22235.00 Issue Date: 12/19/2025
Scale: 1/8" = 1'-0" Phase: CD
Print Date: 12/18/2025 3:05:04 PM
No. Date Description
1 12/19/2025 PERMIT SET

**OVERALL FLOOR
PLAN - LEVEL 1**

A2.01

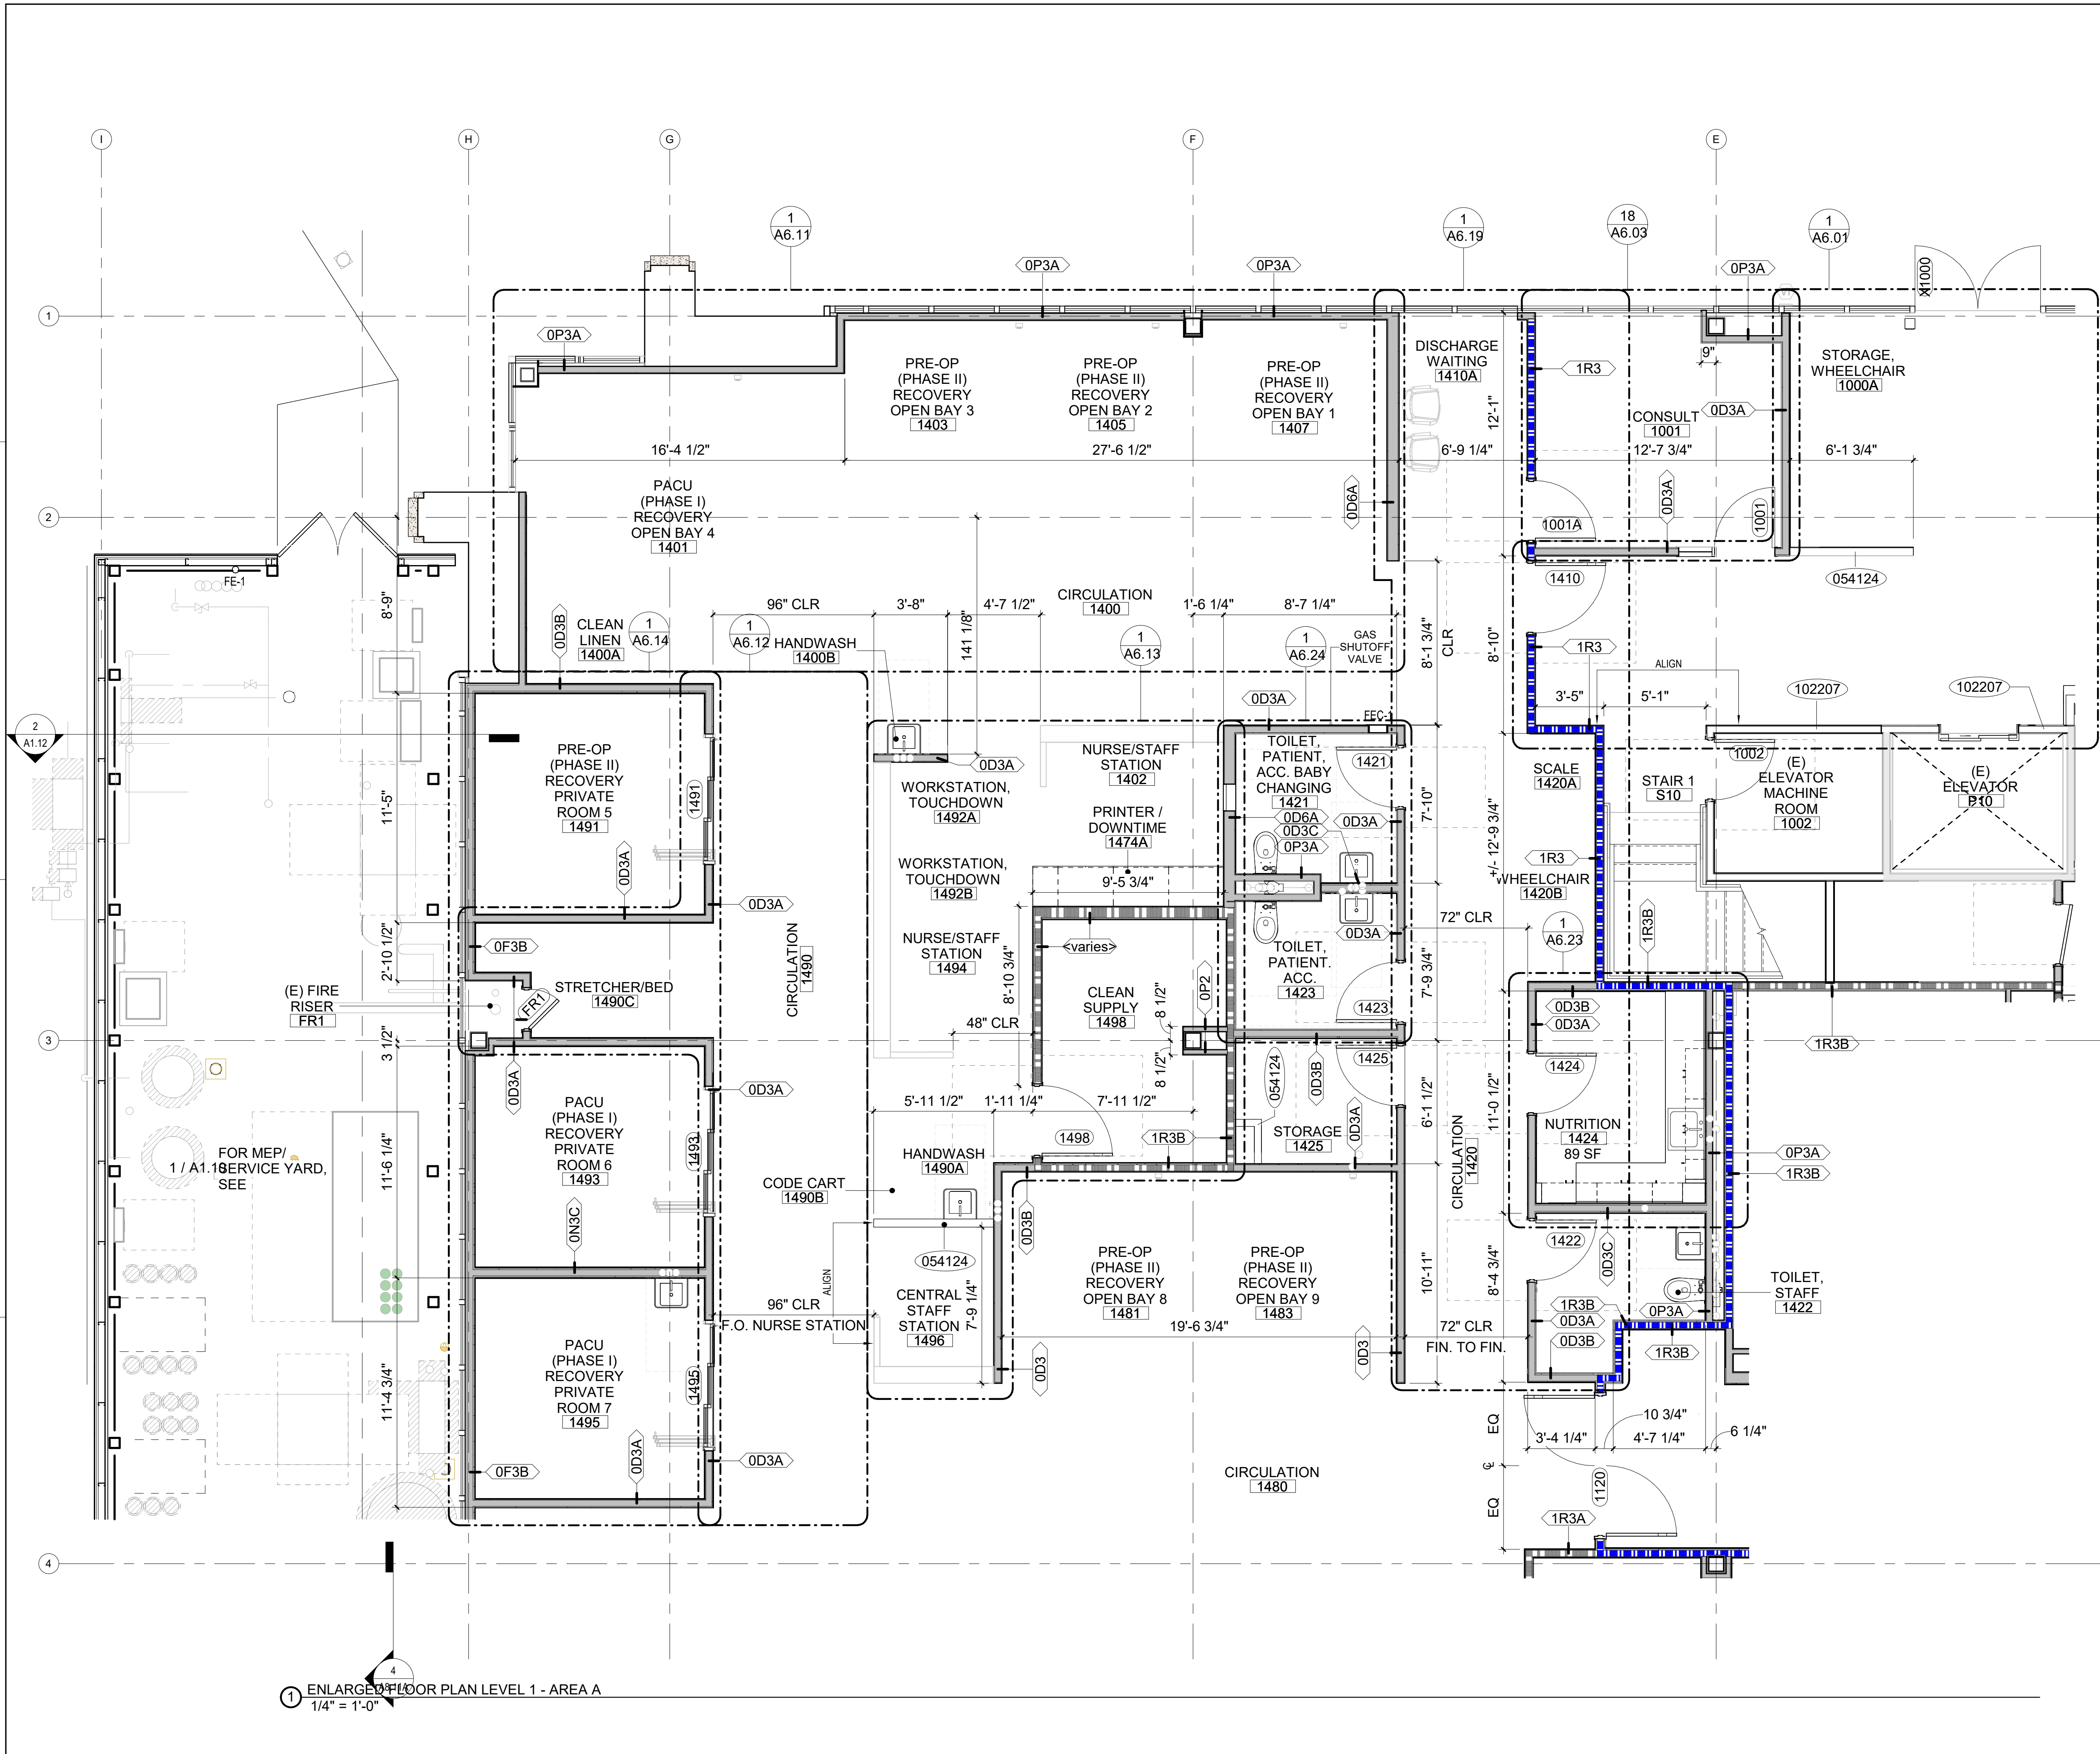

1 ENLARGED FLOOR PLAN LEVEL 1 - AREA A
1/4" = 1'-0"

GENERAL PLAN NOTES



- CONTRACTOR TO NOTIFY ARCHITECT OF ANY DISCREPANCY BETWEEN (E) CONDITIONS AND DRAWINGS PRIOR TO PROCEEDING WITH CONSTRUCTION WORK.
- SEE STRUCTURAL, TECHNOLOGY, MEP DWGS FOR EXTENT OF WORK.
- SEE SHEET A1 SERIES, CIVIL & LANDSCAPE DWGS. FOR SITE PLAN AND THE EXTENT OF WORK AROUND THE BUILDING
- SEE SIGNAGE SHEET SERIES SG FOR SIGNAGE INFORMATION
- CONTRACTOR TO COORDINATE FIRE SPRINKLER AND FIRE ALARM SYSTEM.
- EMERGENCY OUTLETS AND NURSE CALL SHOWN ON ELEC AND TECH DWGS
- SEE G4.01, G4.02, G4.03, & G4.04 FOR TYP. MOUNTING HTS., PROVIDE BLOCKING FOR ALL WALL MOUNTED ITEMS PER DETAILS
- SEE SHEET A2.31, A2.32, A9.05 FOR FINISHES AND A9.06 FOR TYP. RESTROOM ACCESSORIES. SEE A2.33 FOR FURNITURE
- SEE A4.01 SERIES AND A4.02 FOR RCPS.
- SEE A9.03A-C FOR EQPT. SCHDL AND A9.06 FOR IT EQPT SCHDL
- ALL WALLS 0D3A U.O.N. ON A2.01A-A2.01F

KEYNOTES

#	NOTE
054124	48"H MTL STUD PONY WALL
102207	1-HR RATED PARTITION AT(E) ELEVATOR MACHINE ROOM & ELEVATOR SHAFT. CONTRACTOR TO V.I.F.

LEGEND

- NEW 1-HOUR RATED FIRE SMOKE BARRIER
NEW 1-HOUR RATED FIRE BARRIER
EXISTING PARTITION TO REMAIN
NEW UNRATED PARTITION
CUT AND PATCH (E) TPO ROOF

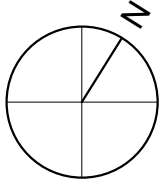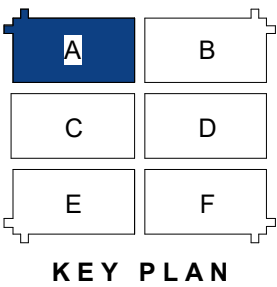

1420 SUTTER ST
SAN FRANCISCO, CA 94109
T 415.391.7918 F 415.391.7309
TEFarch.com



CONSULTANTS:
STRUCTURAL: FORELL|ELSESSER
CIVIL: SANDIS
LANDSCAPE: CREO
LOW VOLTAGE: INTROBA
ACOUSTICAL: SALTER
CODE: JENSEN HUGHES

SHC Hacienda Lakes Ambulatory Surgical Center


4457 Willow Rd
Pleasanton, CA



Project Number	22235.00	Issue Date	12/19/2025
Scale	As indicated	Phase	CD
Print Date	12/18/2025 3:05:07 PM		
No.	Date	Description	
1	12/19/2025	PERMIT SET	

ENLARGED LEVEL 1 FLOOR PLAN - AREA A

A2.01A

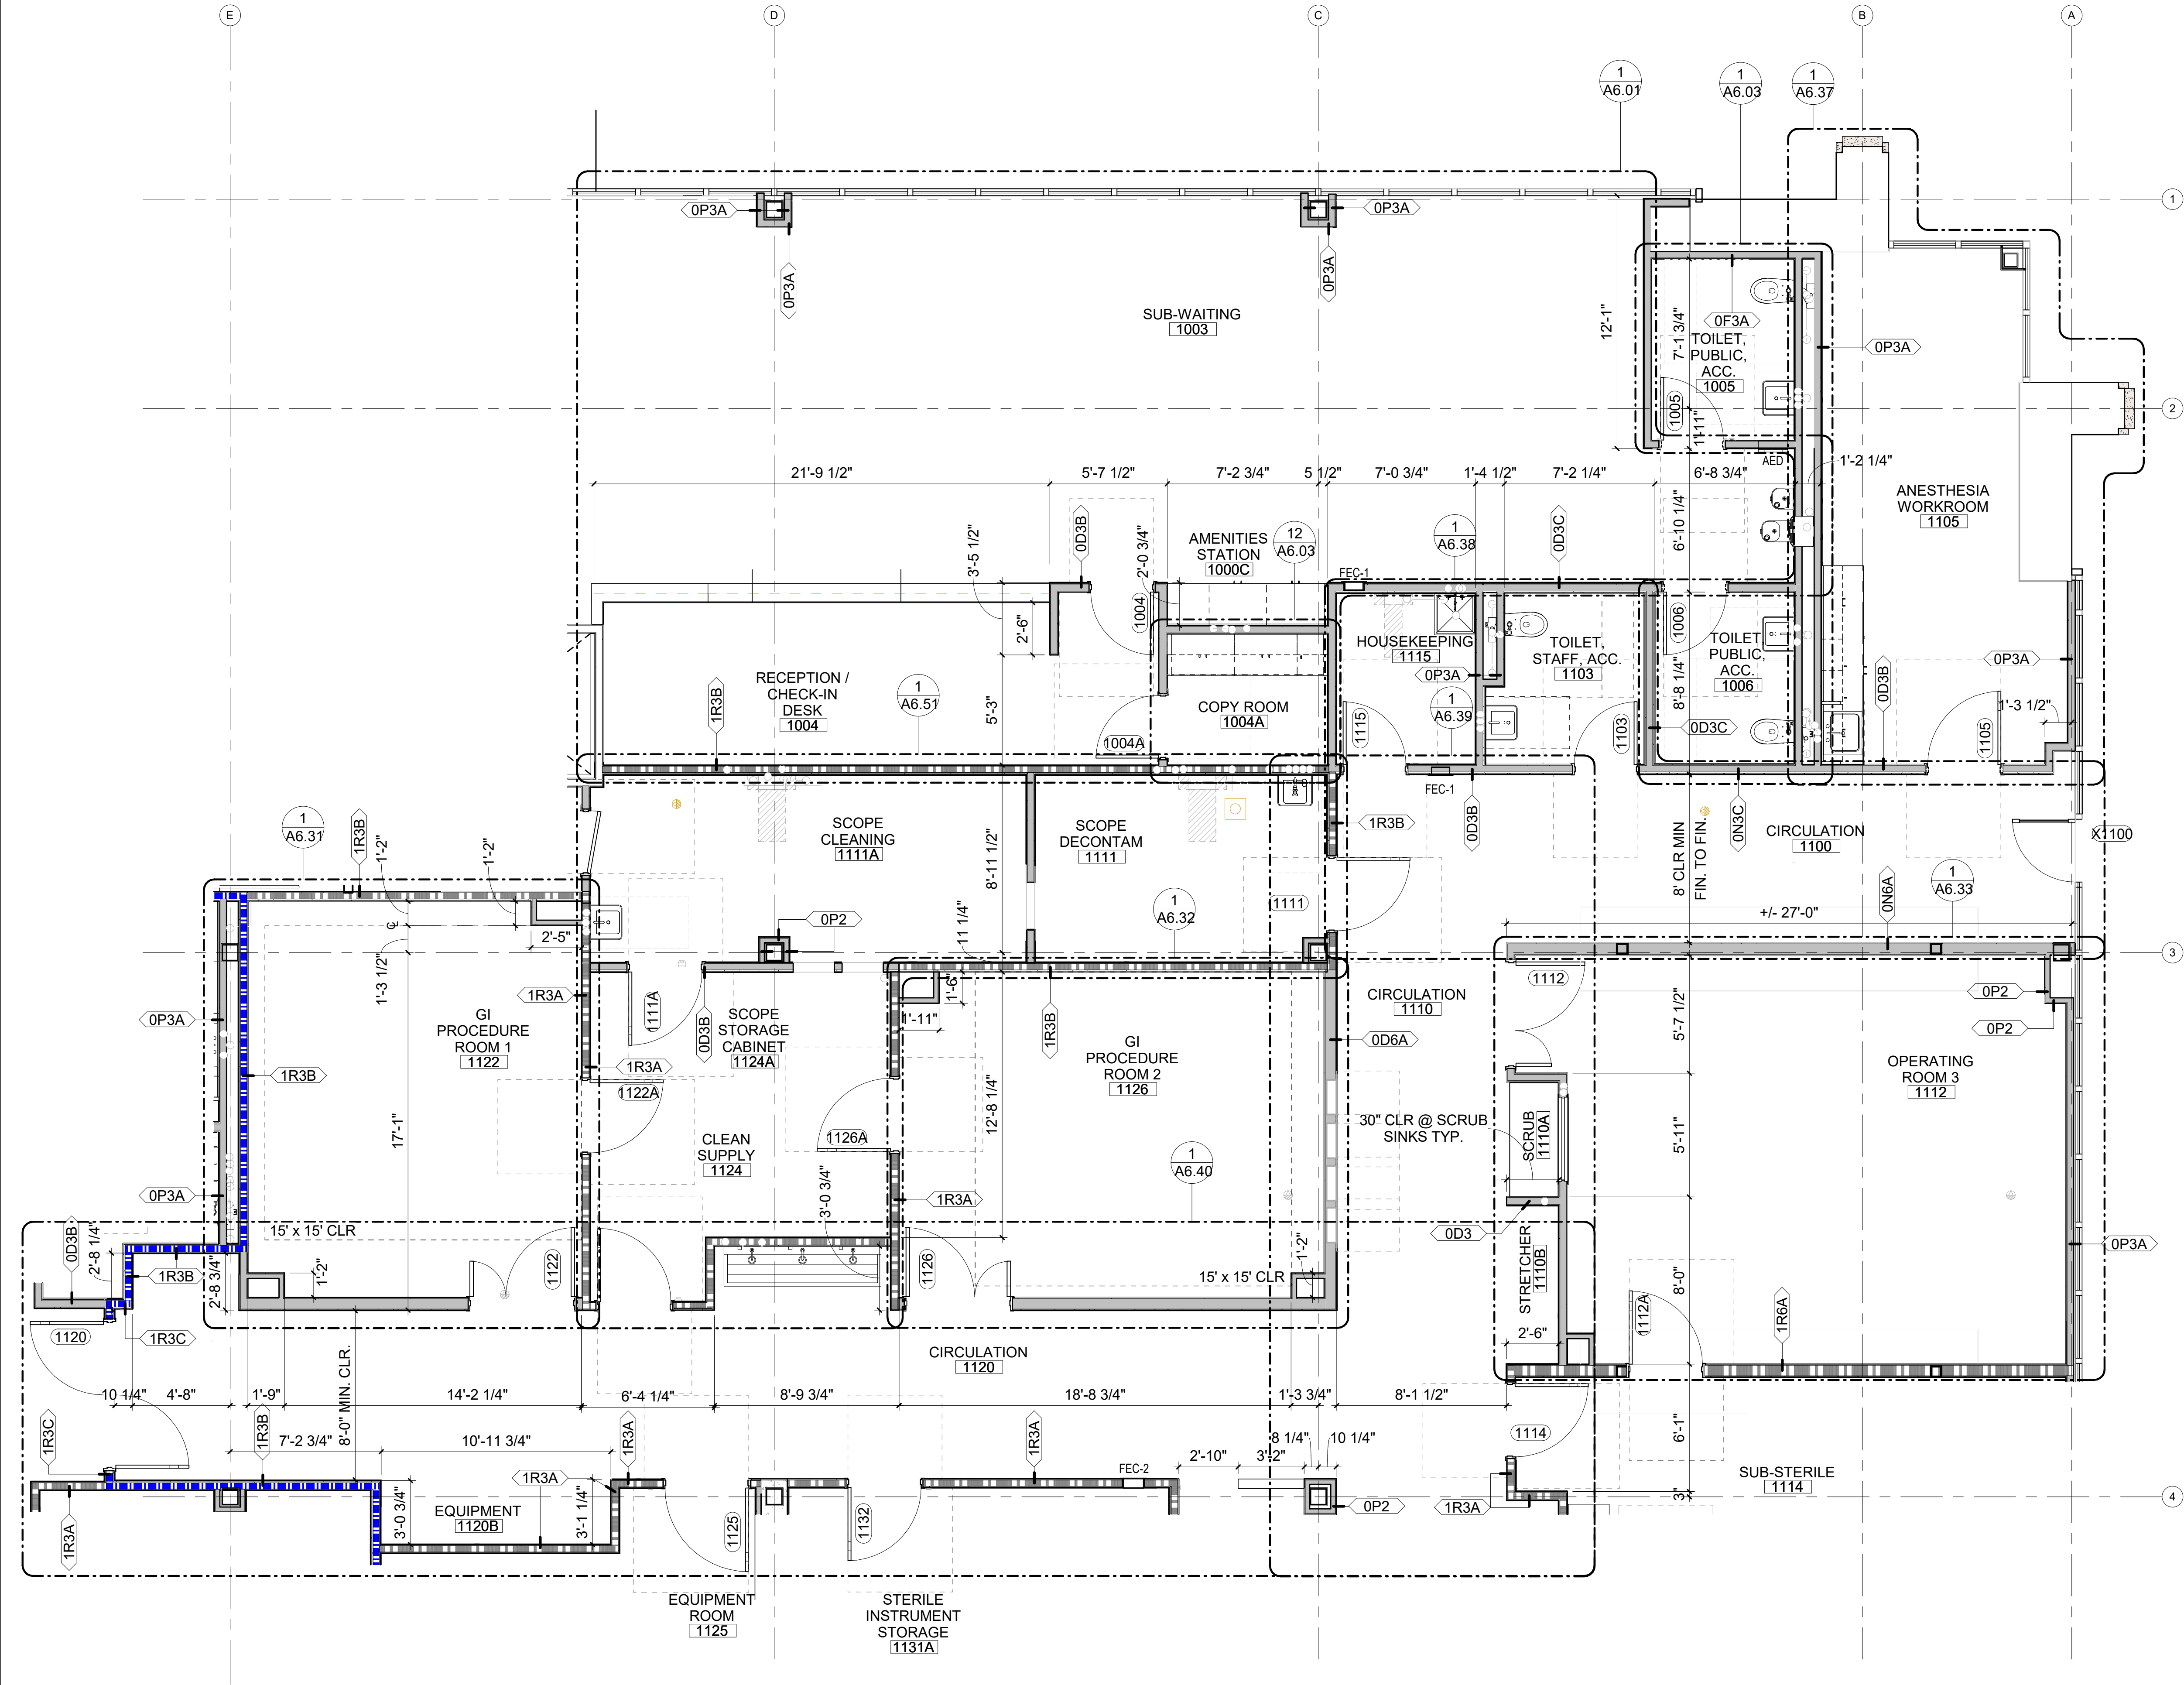

1 ENLARGED FLOOR PLAN LEVEL 1 - AREA B
1/4" = 1'-0"

All drawings and written material appearing herein constitute original and unpublished work of the Architect and may not be duplicated, used or disclosed without consent of Architect.

If this drawing is not 24" x 36", then the drawing has been revised from its original size. Noted scales must be adjusted. This line should be equal to one inch.

GENERAL PLAN NOTES



- CONTRACTOR TO NOTIFY ARCHITECT OF ANY DISCREPANCY BETWEEN (E) CONDITIONS AND DRAWINGS PRIOR TO PROCEEDING WITH CONSTRUCTION WORK.
- SEE STRUCTURAL, TECHNOLOGY, MEP DWGS FOR EXTENT OF WORK.
- SEE SHEET A1 SERIES, CIVIL & LANDSCAPE DWGS. FOR SITE PLAN AND THE EXTENT OF WORK AROUND THE BUILDING
- SEE SIGNAGE SHEET SERIES SG FOR SIGNAGE INFORMATION
- CONTRACTOR TO COORDINATE FIRE SPRINKLER AND FIRE ALARM SYSTEM.
- EMERGENCY OUTLETS AND NURSE CALL SHOWN ON ELEC AND TECH DWGS
- SEE G4.01, G4.02, G4.03, & G4.04 FOR TYP. MOUNTING HTS., PROVIDE BLOCKING FOR ALL WALL MOUNTED ITEMS PER DETAILS
- SEE SHEET A2.31, A2.32, A9.05 FOR FINISHES AND A9.06 FOR TYP. RESTROOM ACCESSORIES. SEE A2.33 FOR FURNITURE
- SEE A4.01 SERIES AND A4.02 FOR RCPS.
- SEE A9.03A-C FOR EQPT. SCHDL AND A9.06 FOR IT EQPT SCHDL
- ALL WALLS 0D3A U.O.N. ON A2.01A-A2.01F

KEYNOTES

#	NOTE
---	------

LEGEND

- NEW 1-HOUR RATED FIRE SMOKE BARRIER
NEW 1-HOUR RATED FIRE BARRIER
EXISTING PARTITION TO REMAIN
NEW UNRATED PARTITION
CUT AND PATCH (E) TPO ROOF

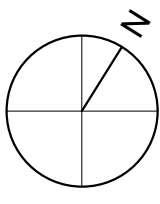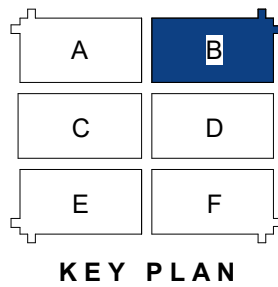

1420 SUTTER ST
SAN FRANCISCO, CA 94109
T 415.391.7918 F 415.391.7309
TEFarch.com



CONSULTANTS:
STRUCTURAL: FORELL|ELSESSER
CIVIL: SANDIS
LANDSCAPE: CREO
LOW VOLTAGE: INTROBA
ACOUSTICAL: SALTER
CODE: JENSEN HUGHES

**SHC Hacienda
Lakes Ambulatory
Surgical Center**


4457 Willow Rd
Pleasanton, CA



Project Number	22235.00	Issue Date	12/19/2025
Scale	As indicated	Phase	CD
Print Date	12/18/2025 3:05:11 PM		
No.	Date	Description	
1	12/19/2025	PERMIT SET	

**ENLARGED LEVEL 1
FLOOR PLAN - AREA
B**

A2.01B

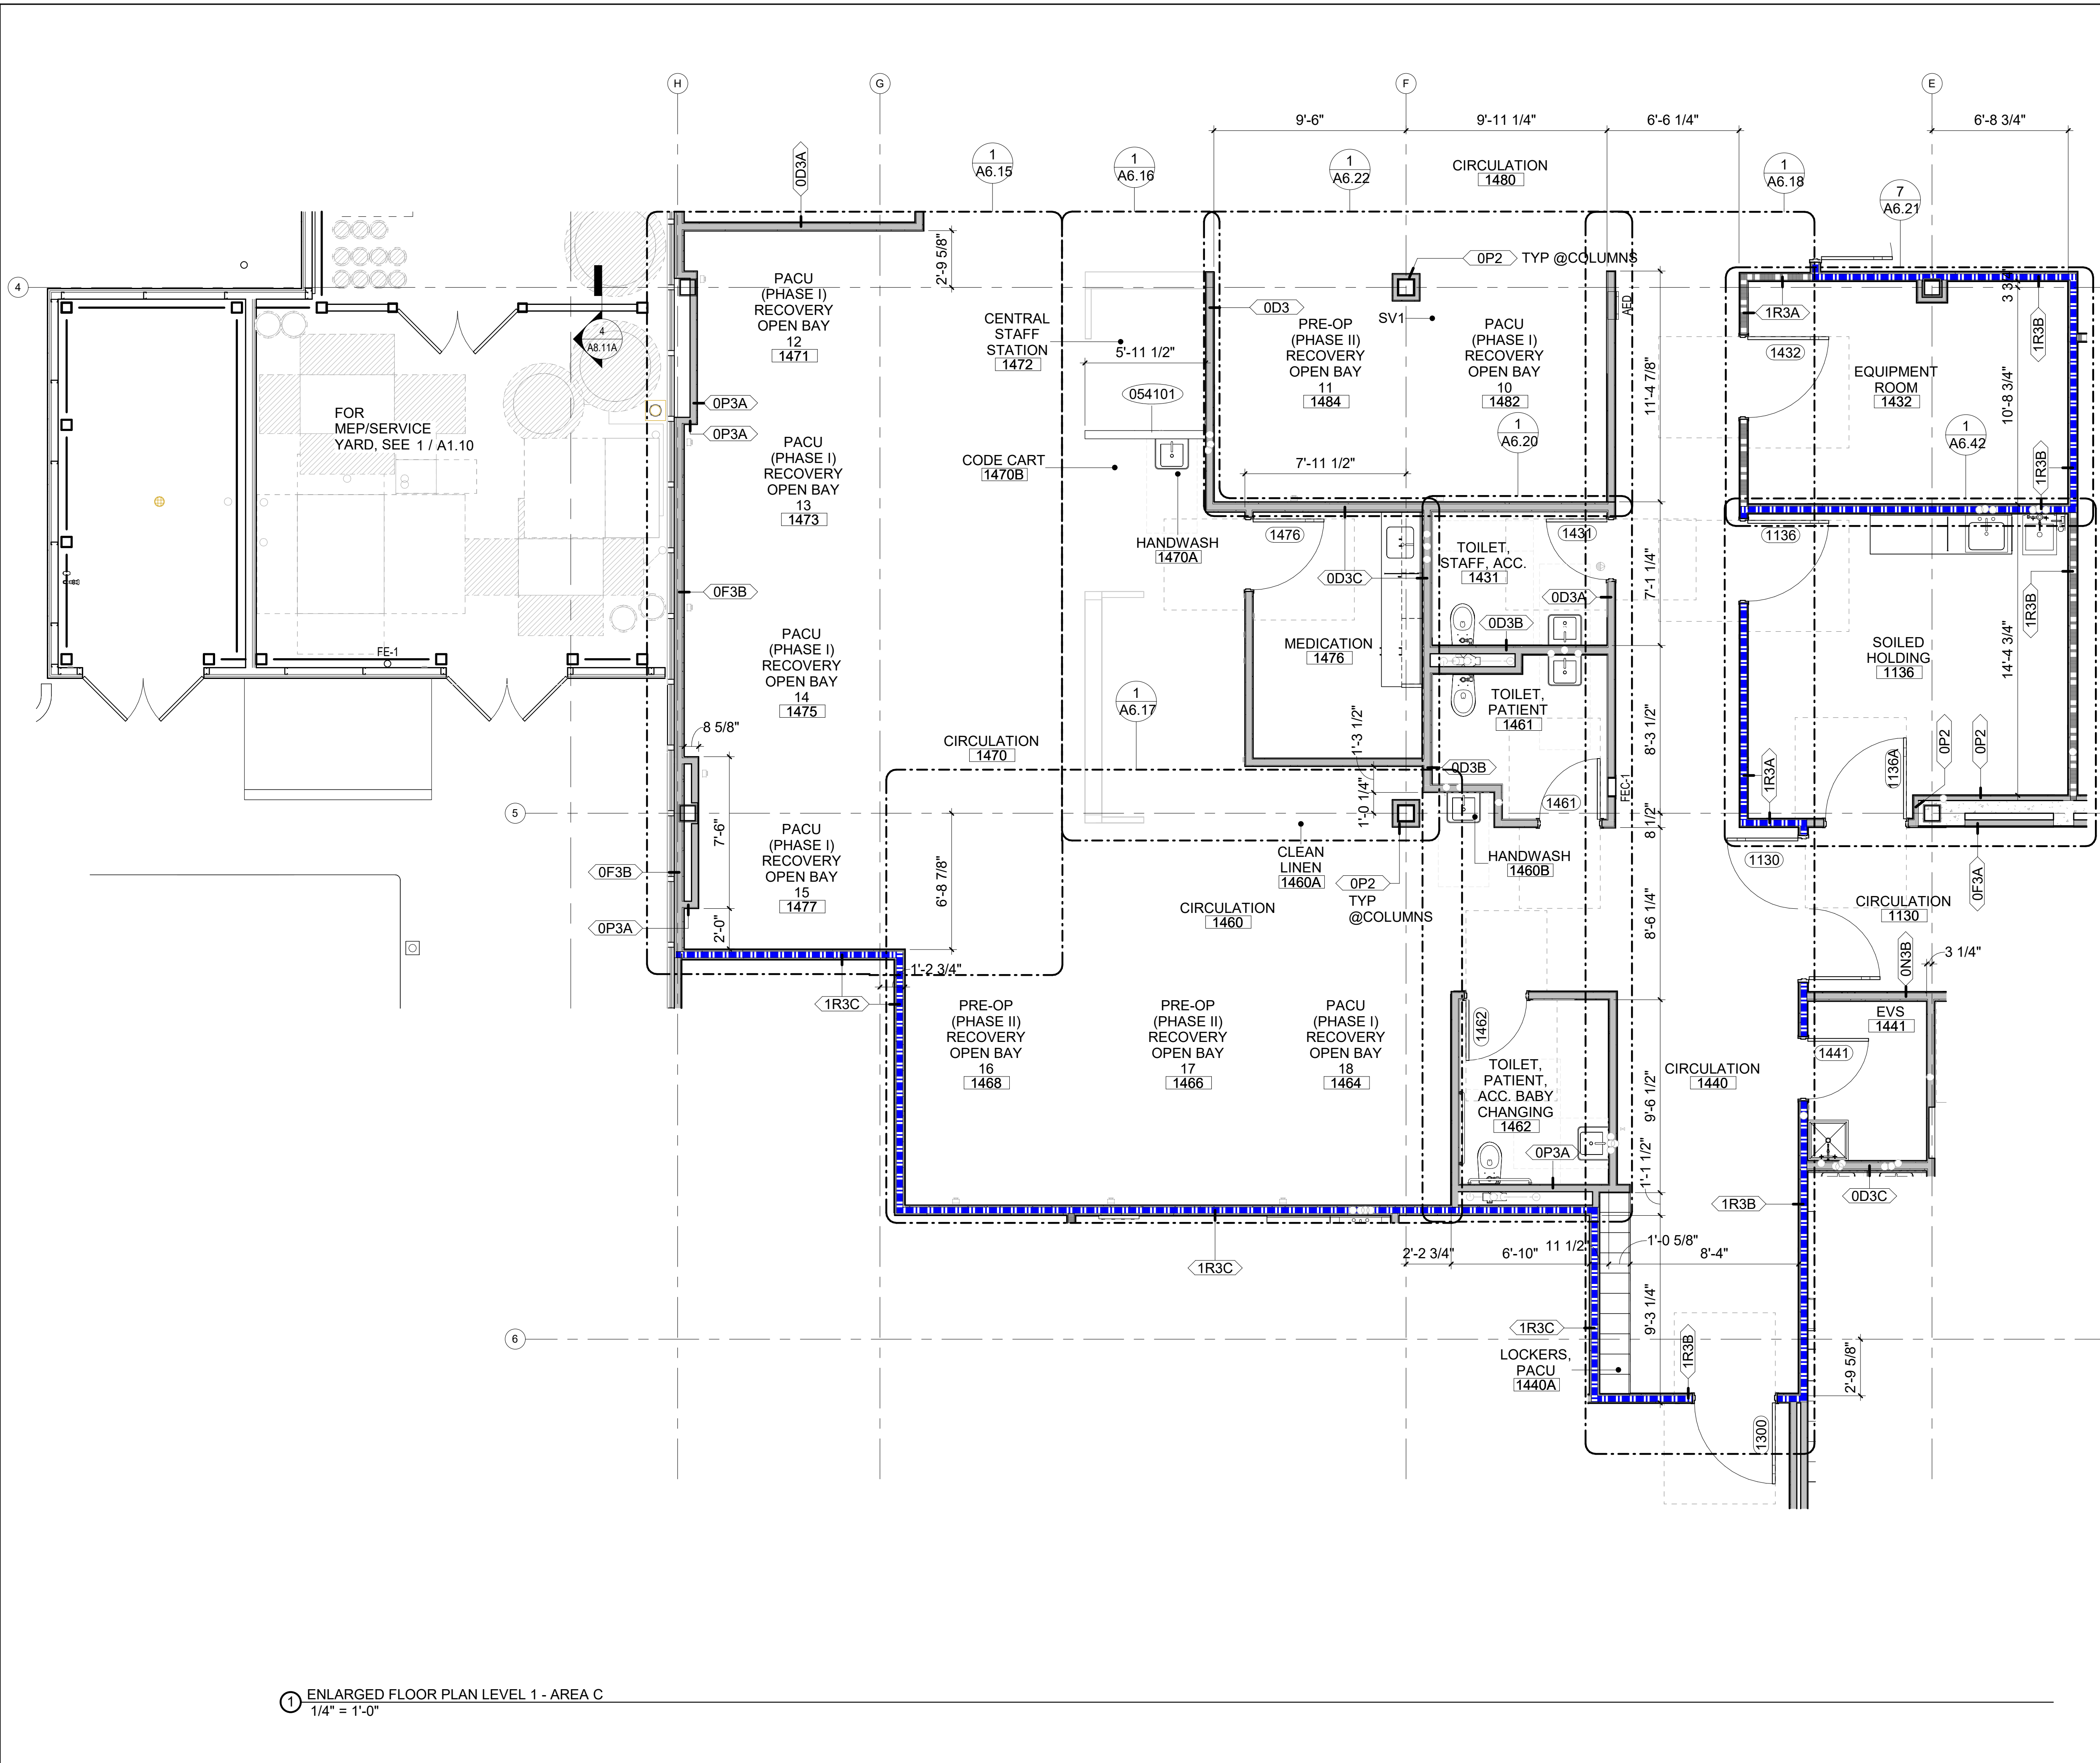

1 ENLARGED FLOOR PLAN LEVEL 1 - AREA C
1/4" = 1'-0"

All drawings and written material appearing herein constitute original and unpublished work of the Architect and may not be duplicated, used or disclosed without consent of Architect.

If this drawing is not 24" x 36", then the drawing has been revised from its original size. Noted scales must be adjusted. This line should be equal to one inch.

GENERAL PLAN NOTES


- CONTRACTOR TO NOTIFY ARCHITECT OF ANY DISCREPANCY BETWEEN (E) CONDITIONS AND DRAWINGS PRIOR TO PROCEEDING WITH CONSTRUCTION WORK.
- SEE STRUCTURAL, TECHNOLOGY, MEP DWGS FOR EXTENT OF WORK.
- SEE SHEET A1 SERIES, CIVIL & LANDSCAPE DWGS. FOR SITE PLAN AND THE EXTENT OF WORK AROUND THE BUILDING
- SEE SIGNAGE SHEET SERIES SG FOR SIGNAGE INFORMATION
- CONTRACTOR TO COORDINATE FIRE SPRINKLER AND FIRE ALARM SYSTEM.
- EMERGENCY OUTLETS AND NURSE CALL SHOWN ON ELEC AND TECH DWGS.
- SEE G4.01, G4.02, G4.03, & G4.04 FOR TYP. MOUNTING HTS., PROVIDE BLOCKING FOR ALL WALL MOUNTED ITEMS PER DETAILS
- SEE SHEET A2.31, A2.32, A9.05 FOR FINISHES AND A9.06 FOR TYP. RESTROOM ACCESSORIES. SEE A2.33 FOR FURNITURE
- SEE A4.01 SERIES AND A4.02 FOR RCPS.
- SEE A9.03A-C FOR EQPT. SCHDL AND A9.06 FOR IT EQPT SCHDL
- ALL WALLS 0D3A U.O.N. ON A2.01A-A2.01F

KEYNOTES

#	NOTE
054101	PARTIAL HEIGHT MTL STUD WALL

LEGEND

- NEW 1-HOUR RATED FIRE SMOKE BARRIER
NEW 1-HOUR RATED FIRE BARRIER
EXISTING PARTITION TO REMAIN
NEW UNRATED PARTITION
CUT AND PATCH (E) TPO ROOF

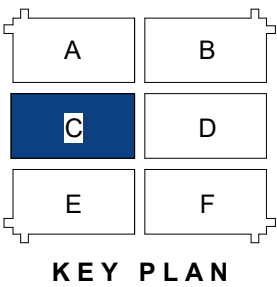

1420 SUTTER ST
SAN FRANCISCO, CA 94109
T 415.391.7918 F 415.391.7309
TEFarch.com



CONSULTANTS:
STRUCTURAL: FORELL|ELSESSER
CIVIL: SANDIS
LANDSCAPE: CREO
LOW VOLTAGE: INTROBA
ACOUSTICAL: SALTER
CODE: JENSEN HUGHES

SHC Hacienda
Lakes Ambulatory
Surgical Center


4457 Willow Rd
Pleasanton, CA



Project Number	22235.00	Issue Date	12/19/2025
Scale	As indicated	Phase	CD
Print Date	12/18/2025 3:05:16 PM		
No.	Date	Description	
1	12/19/2025	PERMIT SET	

ENLARGED LEVEL 1
FLOOR PLAN - AREA
C

A2.01C

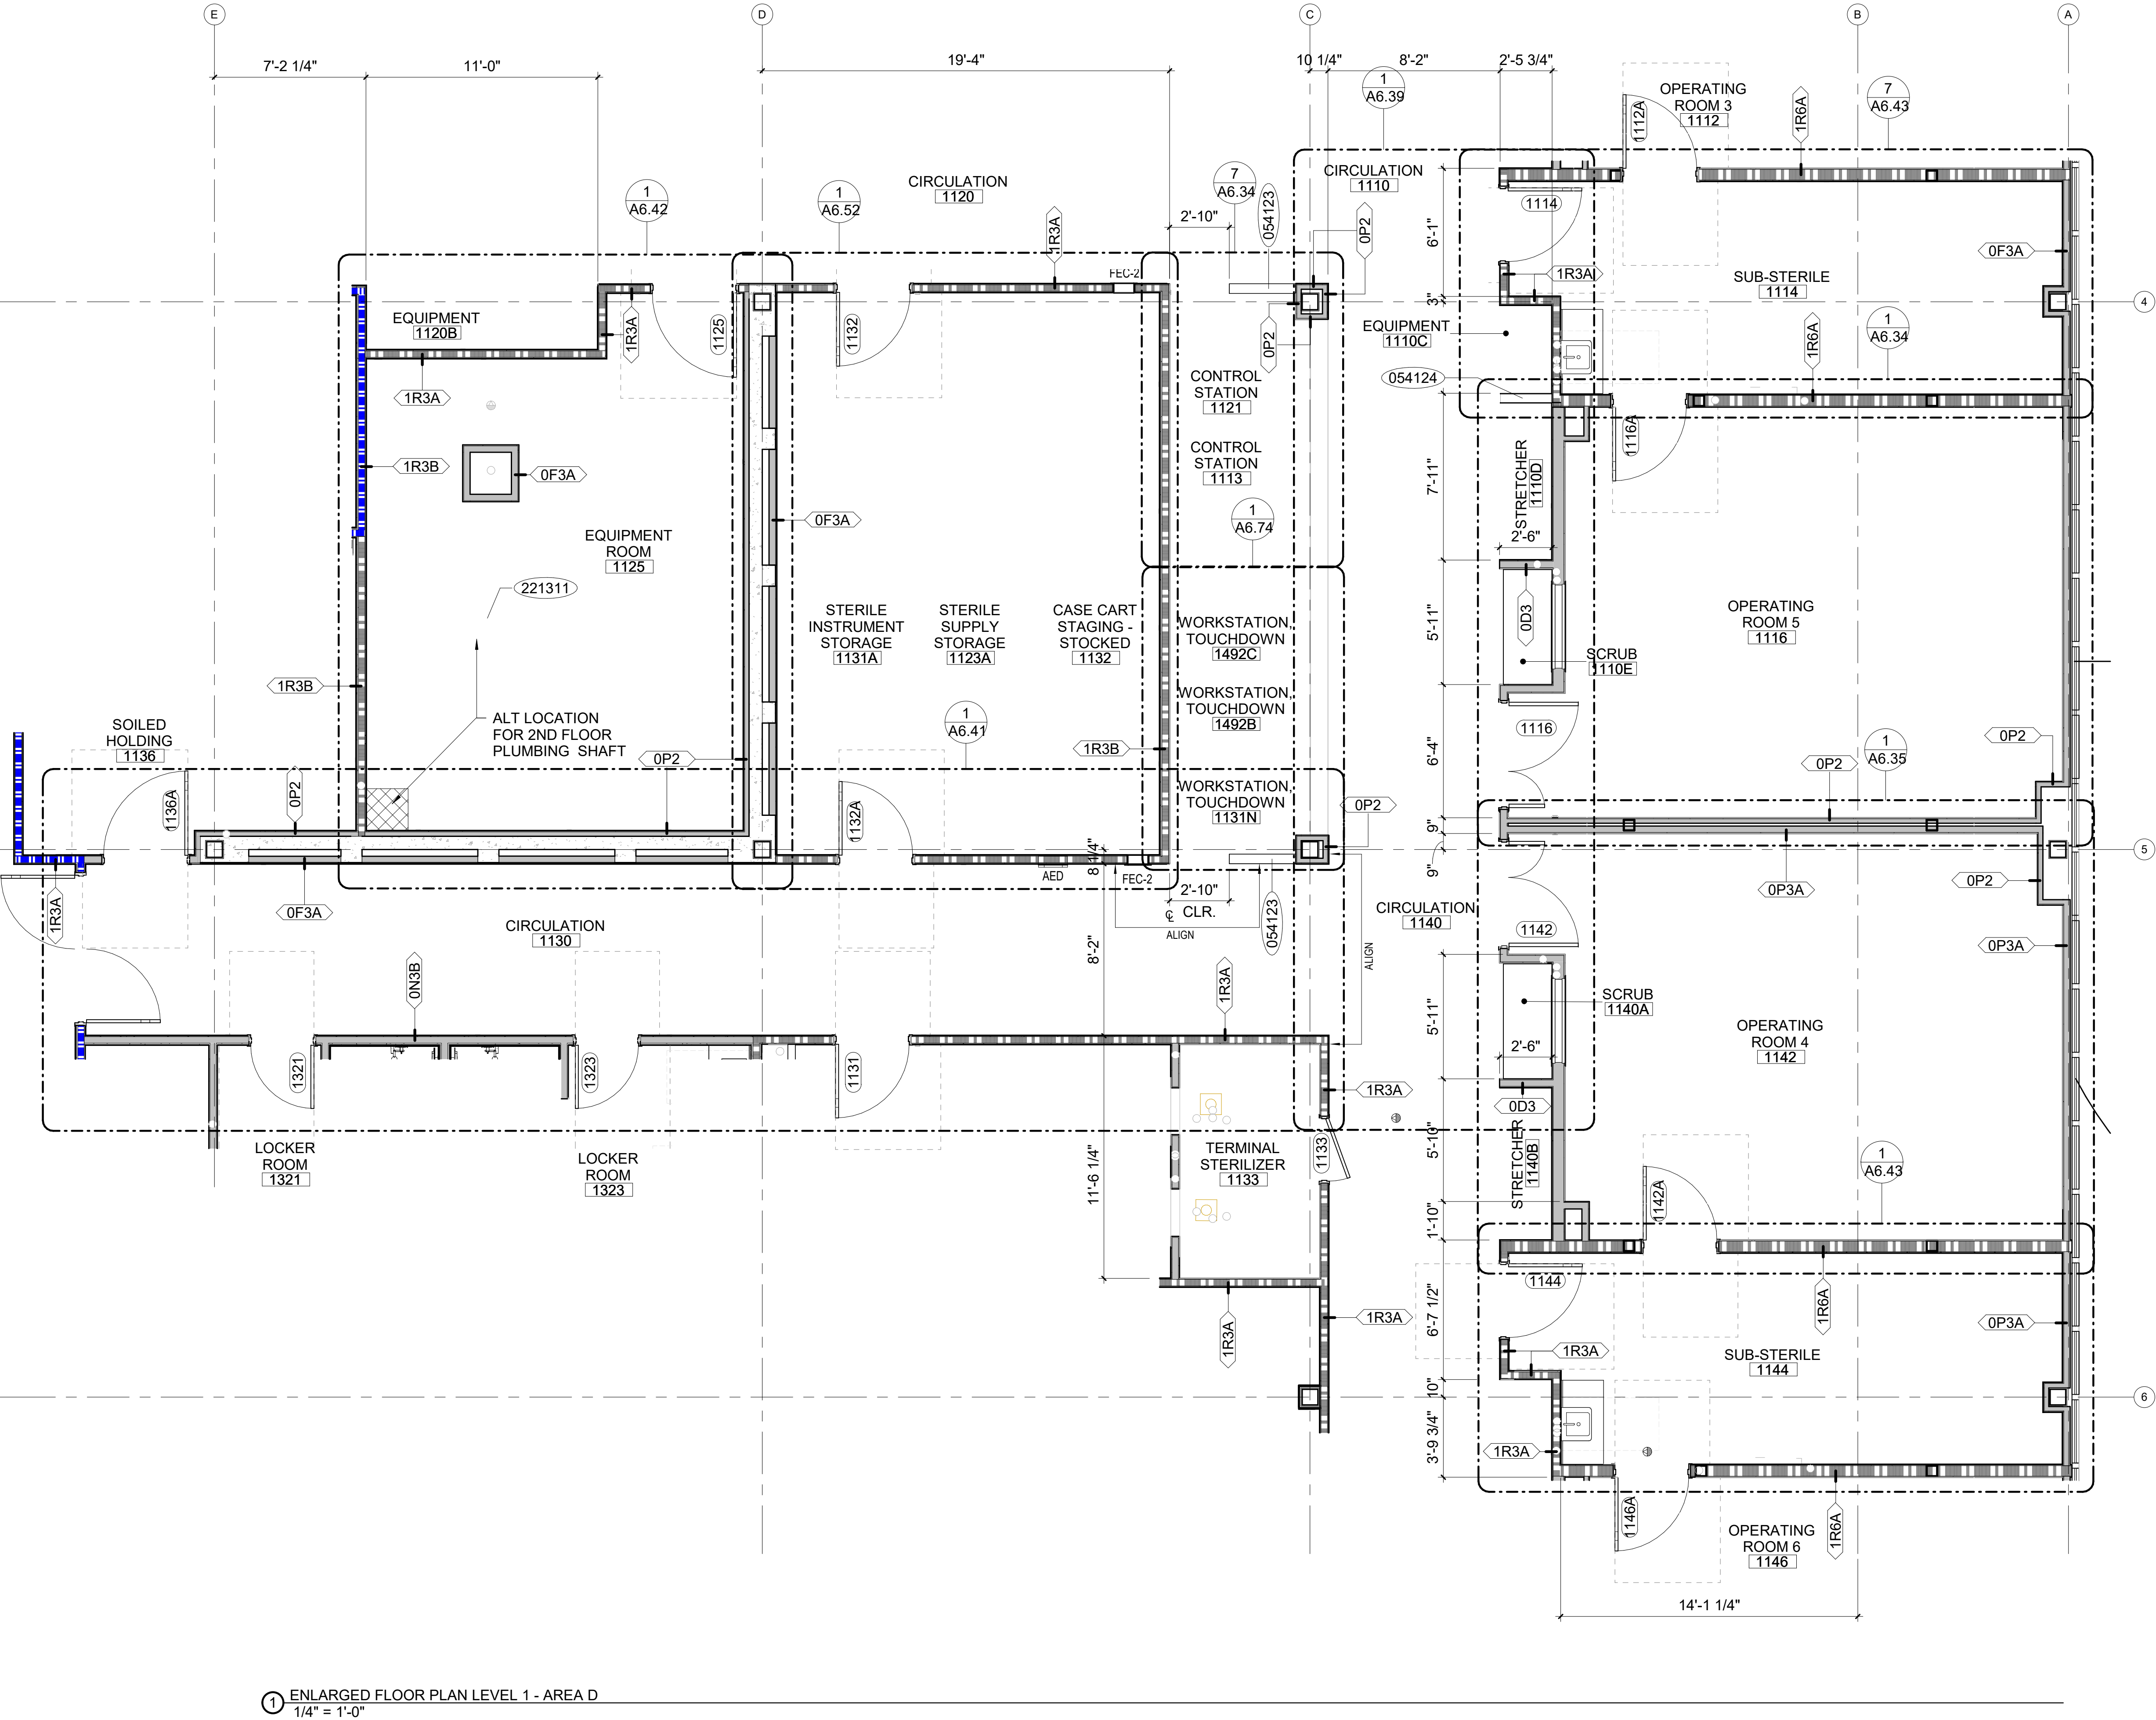

1 ENLARGED FLOOR PLAN LEVEL 1 - AREA D
1/4" = 1'-0"

All drawings and written material appearing herein constitute original and unpublished work of the Architect and may not be duplicated, used or disclosed without consent of Architect.

If this drawing is not 24" x 36", then the drawing has been revised from its original size. Noted scales must be adjusted. This line should be equal to one inch.

GENERAL PLAN NOTES



- CONTRACTOR TO NOTIFY ARCHITECT OF ANY DISCREPANCY BETWEEN (E) CONDITIONS AND DRAWINGS PRIOR TO PROCEEDING WITH CONSTRUCTION WORK.
- SEE STRUCTURAL, TECHNOLOGY, MEP DWGS FOR EXTENT OF WORK.
- SEE SHEET A1 SERIES, CIVIL & LANDSCAPE DWGS. FOR SITE PLAN AND THE EXTENT OF WORK AROUND THE BUILDING
- SEE SIGNAGE SHEET SERIES SG FOR SIGNAGE INFORMATION
- CONTRACTOR TO COORDINATE FIRE SPRINKLER AND FIRE ALARM SYSTEM.
- EMERGENCY OUTLETS AND NURSE CALL SHOWN ON ELEC AND TECH DWGS
- SEE G4.01, G4.02, G4.03, & G4.04 FOR TYP. MOUNTING HTS., PROVIDE BLOCKING FOR ALL WALL MOUNTED ITEMS PER DETAILS
- SEE SHEET A2.31, A2.32, A9.05 FOR FINISHES AND A9.06 FOR TYP. RESTROOM ACCESSORIES. SEE A2.33 FOR FURNITURE
- SEE A4.01 SERIES AND A4.02 FOR RCPS.
- SEE A9.03A-C FOR EQPT. SCHDL AND A9.06 FOR IT EQPT SCHDL
- ALL WALLS 0D3A U.O.N. ON A2.01A-A2.01F

KEYNOTES

#	NOTE
054123	36"H MTL STUD PONY WALL
054124	48"H MTL STUD PONY WALL
221311	PROVIDE PLUMBING SHAFT FOR 2ND FLOOR LINES

LEGEND

- NEW 1-HOUR RATED FIRE SMOKE BARRIER
NEW 1-HOUR RATED FIRE BARRIER
EXISTING PARTITION TO REMAIN
NEW UNRATED PARTITION
CUT AND PATCH (E) TPO ROOF

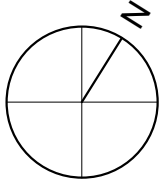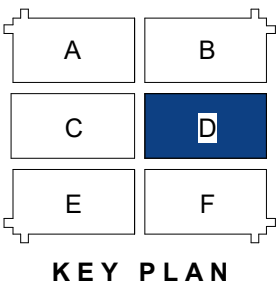

1420 SUTTER ST
SAN FRANCISCO, CA 94109
T 415.391.7918 F 415.391.7309
TEFarch.com



CONSULTANTS:
STRUCTURAL: FORELL|ELSESSER
CIVIL: SANDIS
LANDSCAPE: CREO
LOW VOLTAGE: INTROBA
ACOUSTICAL: SALTER
CODE: JENSEN HUGHES

SHC Hacienda
Lakes Ambulatory
Surgical Center


4457 Willow Rd
Pleasanton, CA



Project Number	22235.00	Issue Date	12/19/2025
Scale	As indicated	Phase	CD
Print Date	12/18/2025 3:05:20 PM		
No.	Date	Description	
1	12/19/2025	PERMIT SET	

ENLARGED LEVEL 1
FLOOR PLAN - AREA
D

A2.01D

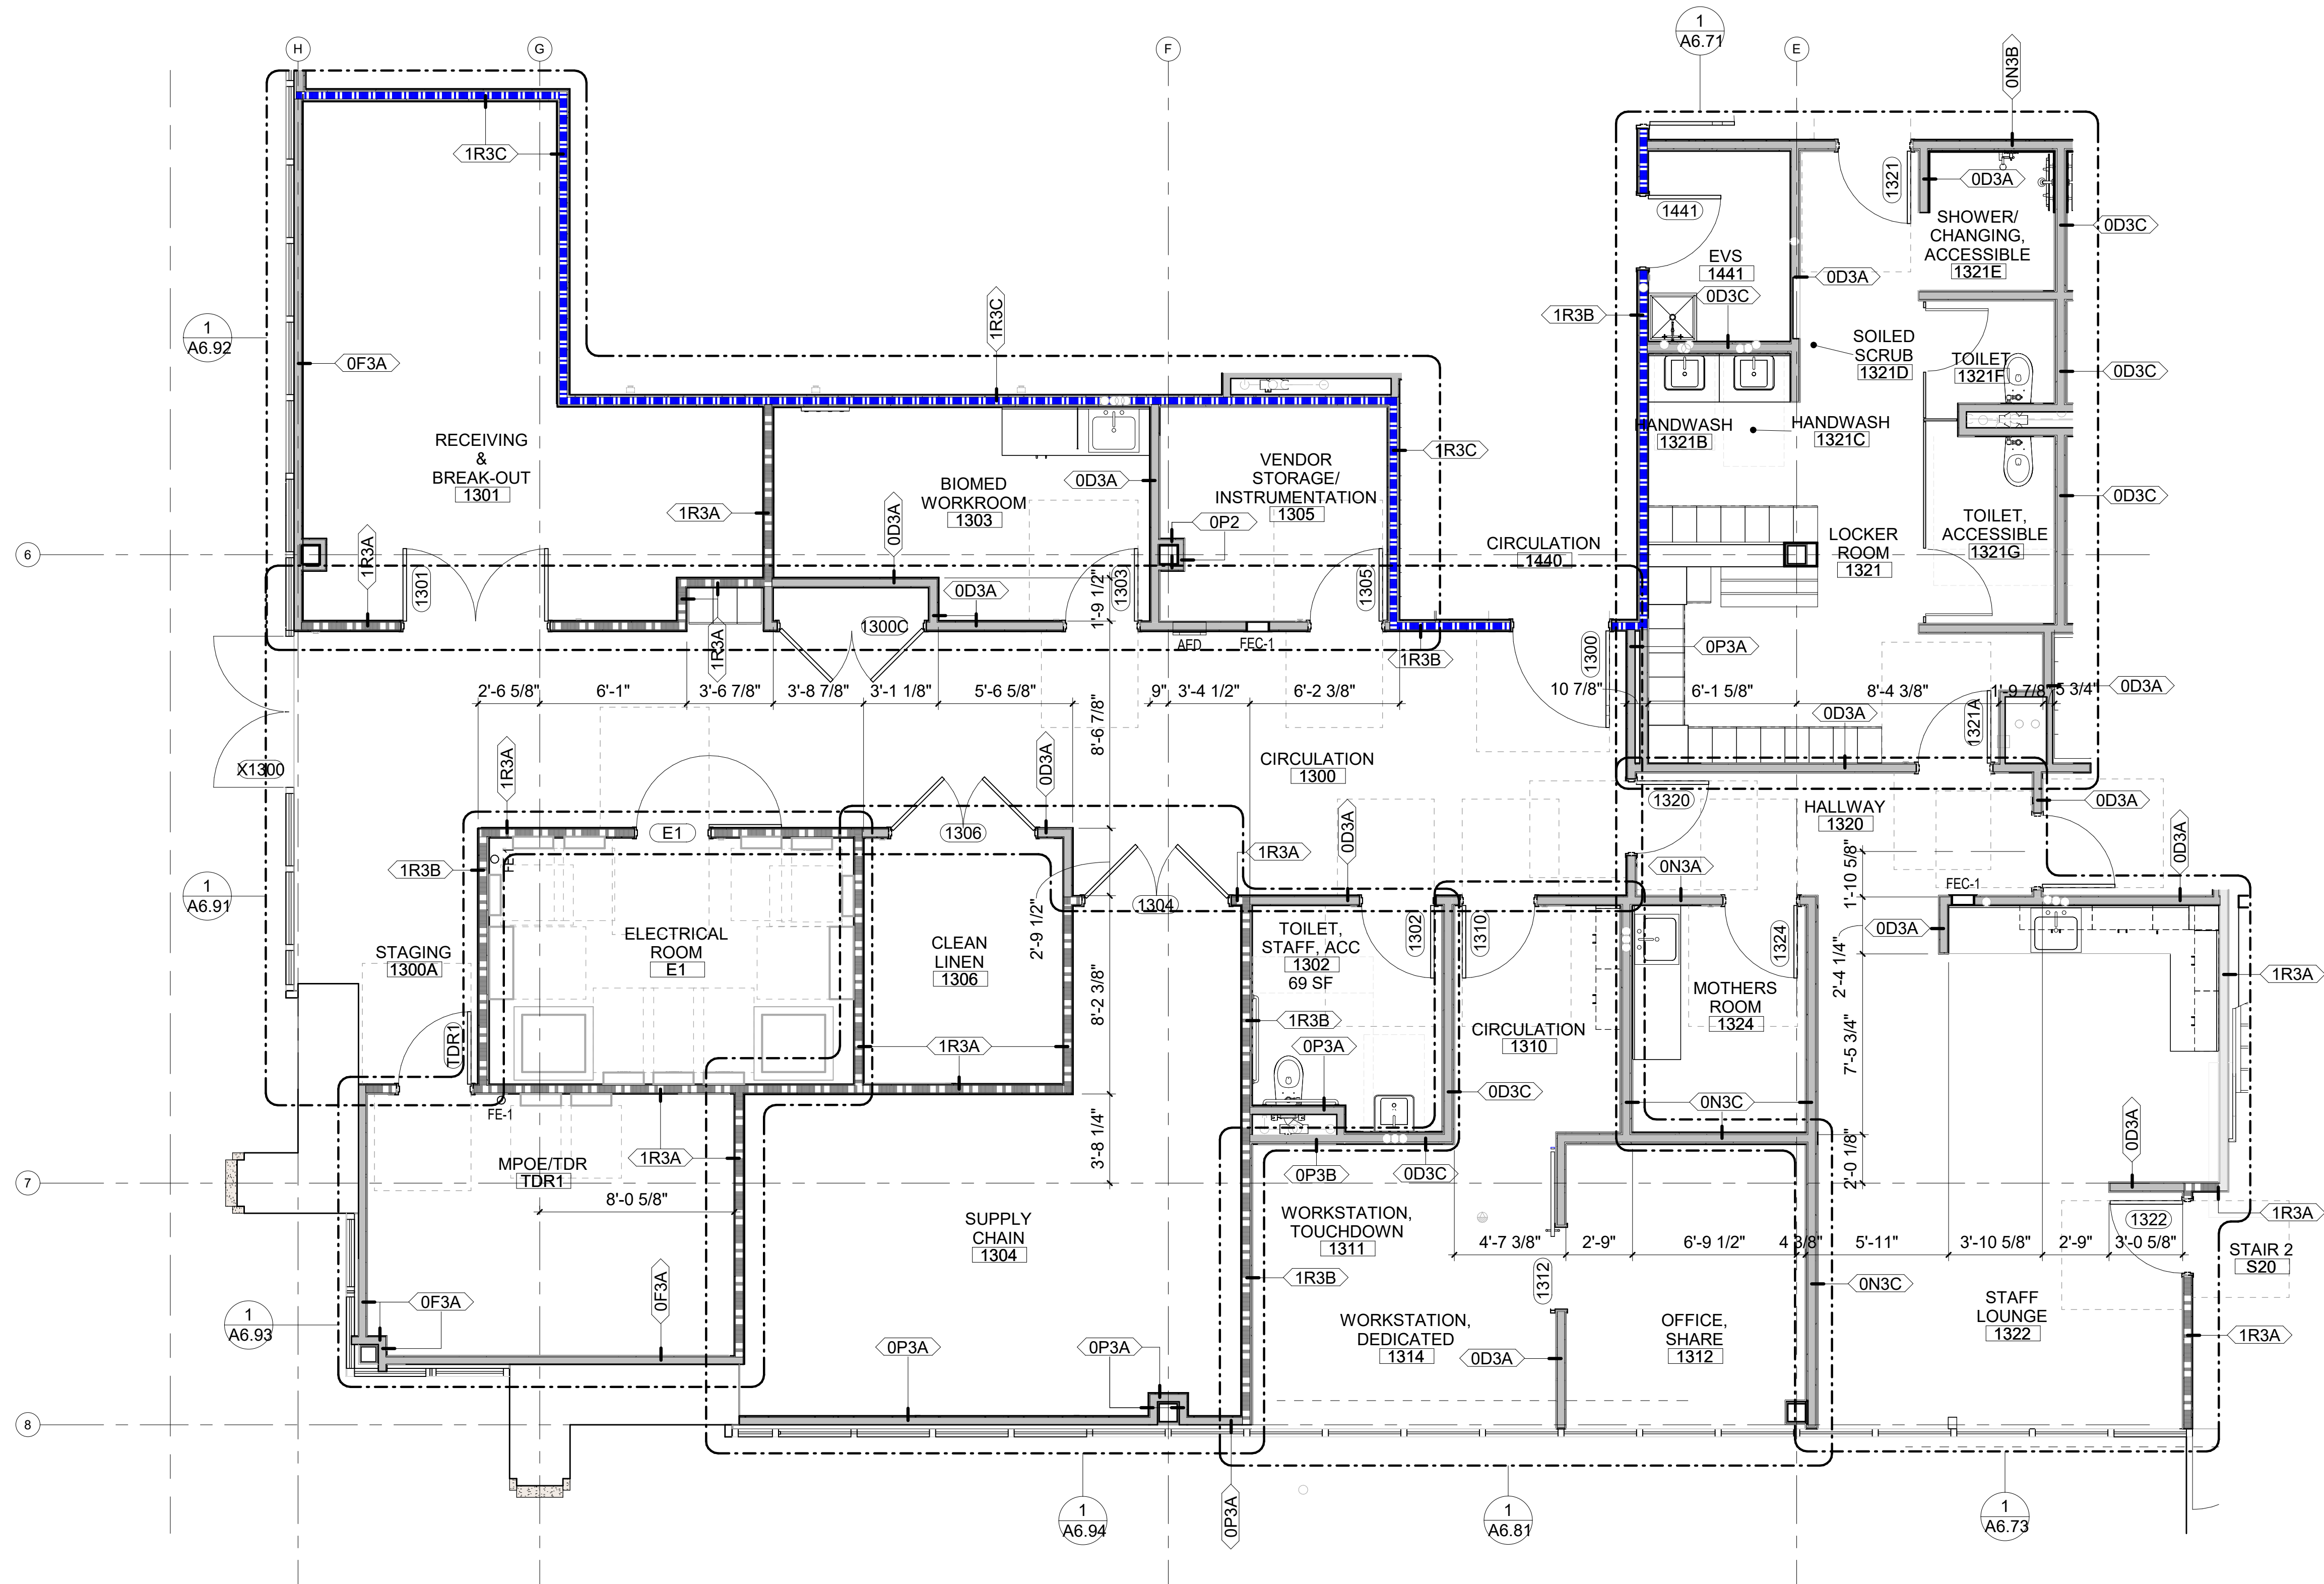

1 ENLARGED FLOOR PLAN LEVEL 1 - AREA E
1/4" = 1'-0"

GENERAL PLAN NOTES



1. CONTRACTOR TO NOTIFY ARCHITECT OF ANY DISCREPANCY BETWEEN (E) CONDITIONS AND DRAWINGS PRIOR TO PROCEEDING WITH CONSTRUCTION WORK.
2. SEE STRUCTURAL, TECHNOLOGY, MEP DWGS FOR EXTENT OF WORK.
3. SEE SHEET A1 SERIES, CIVIL & LANDSCAPE DWGS. FOR SITE PLAN AND THE EXTENT OF WORK AROUND THE BUILDING
4. SEE SIGNAGE SHEET SERIES SG FOR SIGNAGE INFORMATION
5. CONTRACTOR TO COORDINATE FIRE SPRINKLER AND FIRE ALARM SYSTEM.
6. EMERGENCY OUTLETS AND NURSE CALL SHOWN ON ELEC AND TECH DWGS
7. SEE G4.01, G4.02, G4.03, & G4.04 FOR TYP. MOUNTING HTS., PROVIDE BLOCKING FOR ALL WALL MOUNTED ITEMS PER DETAILS
8. SEE SHEET A2.31, A2.32, A9.05 FOR FINISHES AND A9.06 FOR TYP. RESTROOM ACCESSORIES. SEE A2.33 FOR FURNITURE
9. SEE A4.01 SERIES AND A4.02 FOR RCPS.
10. SEE A9.03A-C FOR EQPT. SCHDL AND A9.06 FOR IT EQPT SCHDL
11. ALL WALLS 0D3A U.O.N. ON A2.01A-A2.01F

KEYNOTES

#	NOTE
---	------

LEGEND

- NEW 1-HOUR RATED FIRE SMOKE BARRIER
NEW 1-HOUR RATED FIRE BARRIER
EXISTING PARTITION TO REMAIN
NEW UNRATED PARTITION
CUT AND PATCH (E) TPO ROOF

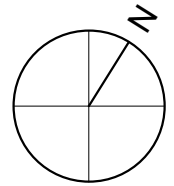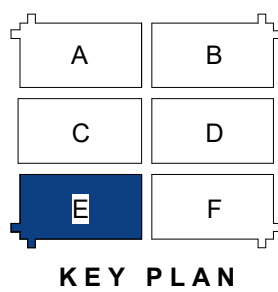

1420 SUTTER ST
SAN FRANCISCO, CA 94109
T 415.391.7918 F 415.391.7309
TEFarch.com



CONSULTANTS:
STRUCTURAL: FORELL|ELSESSER
CIVIL: SANDIS
LANDSCAPE: CREO
LOW VOLTAGE: INTROBA
ACOUSTICAL: SALTER
CODE: JENSEN HUGHES

SHC Hacienda Lakes Ambulatory Surgical Center


4457 Willow Rd
Pleasanton, CA



Project Number	22235.00	Issue Date	12/19/2025
Scale	As indicated	Phase	CD
Print Date	12/18/2025 3:05:24 PM		
No.	Date	Description	
1	12/19/2025	PERMIT SET	

ENLARGED LEVEL 1 FLOOR PLAN - AREA E

A2.01E

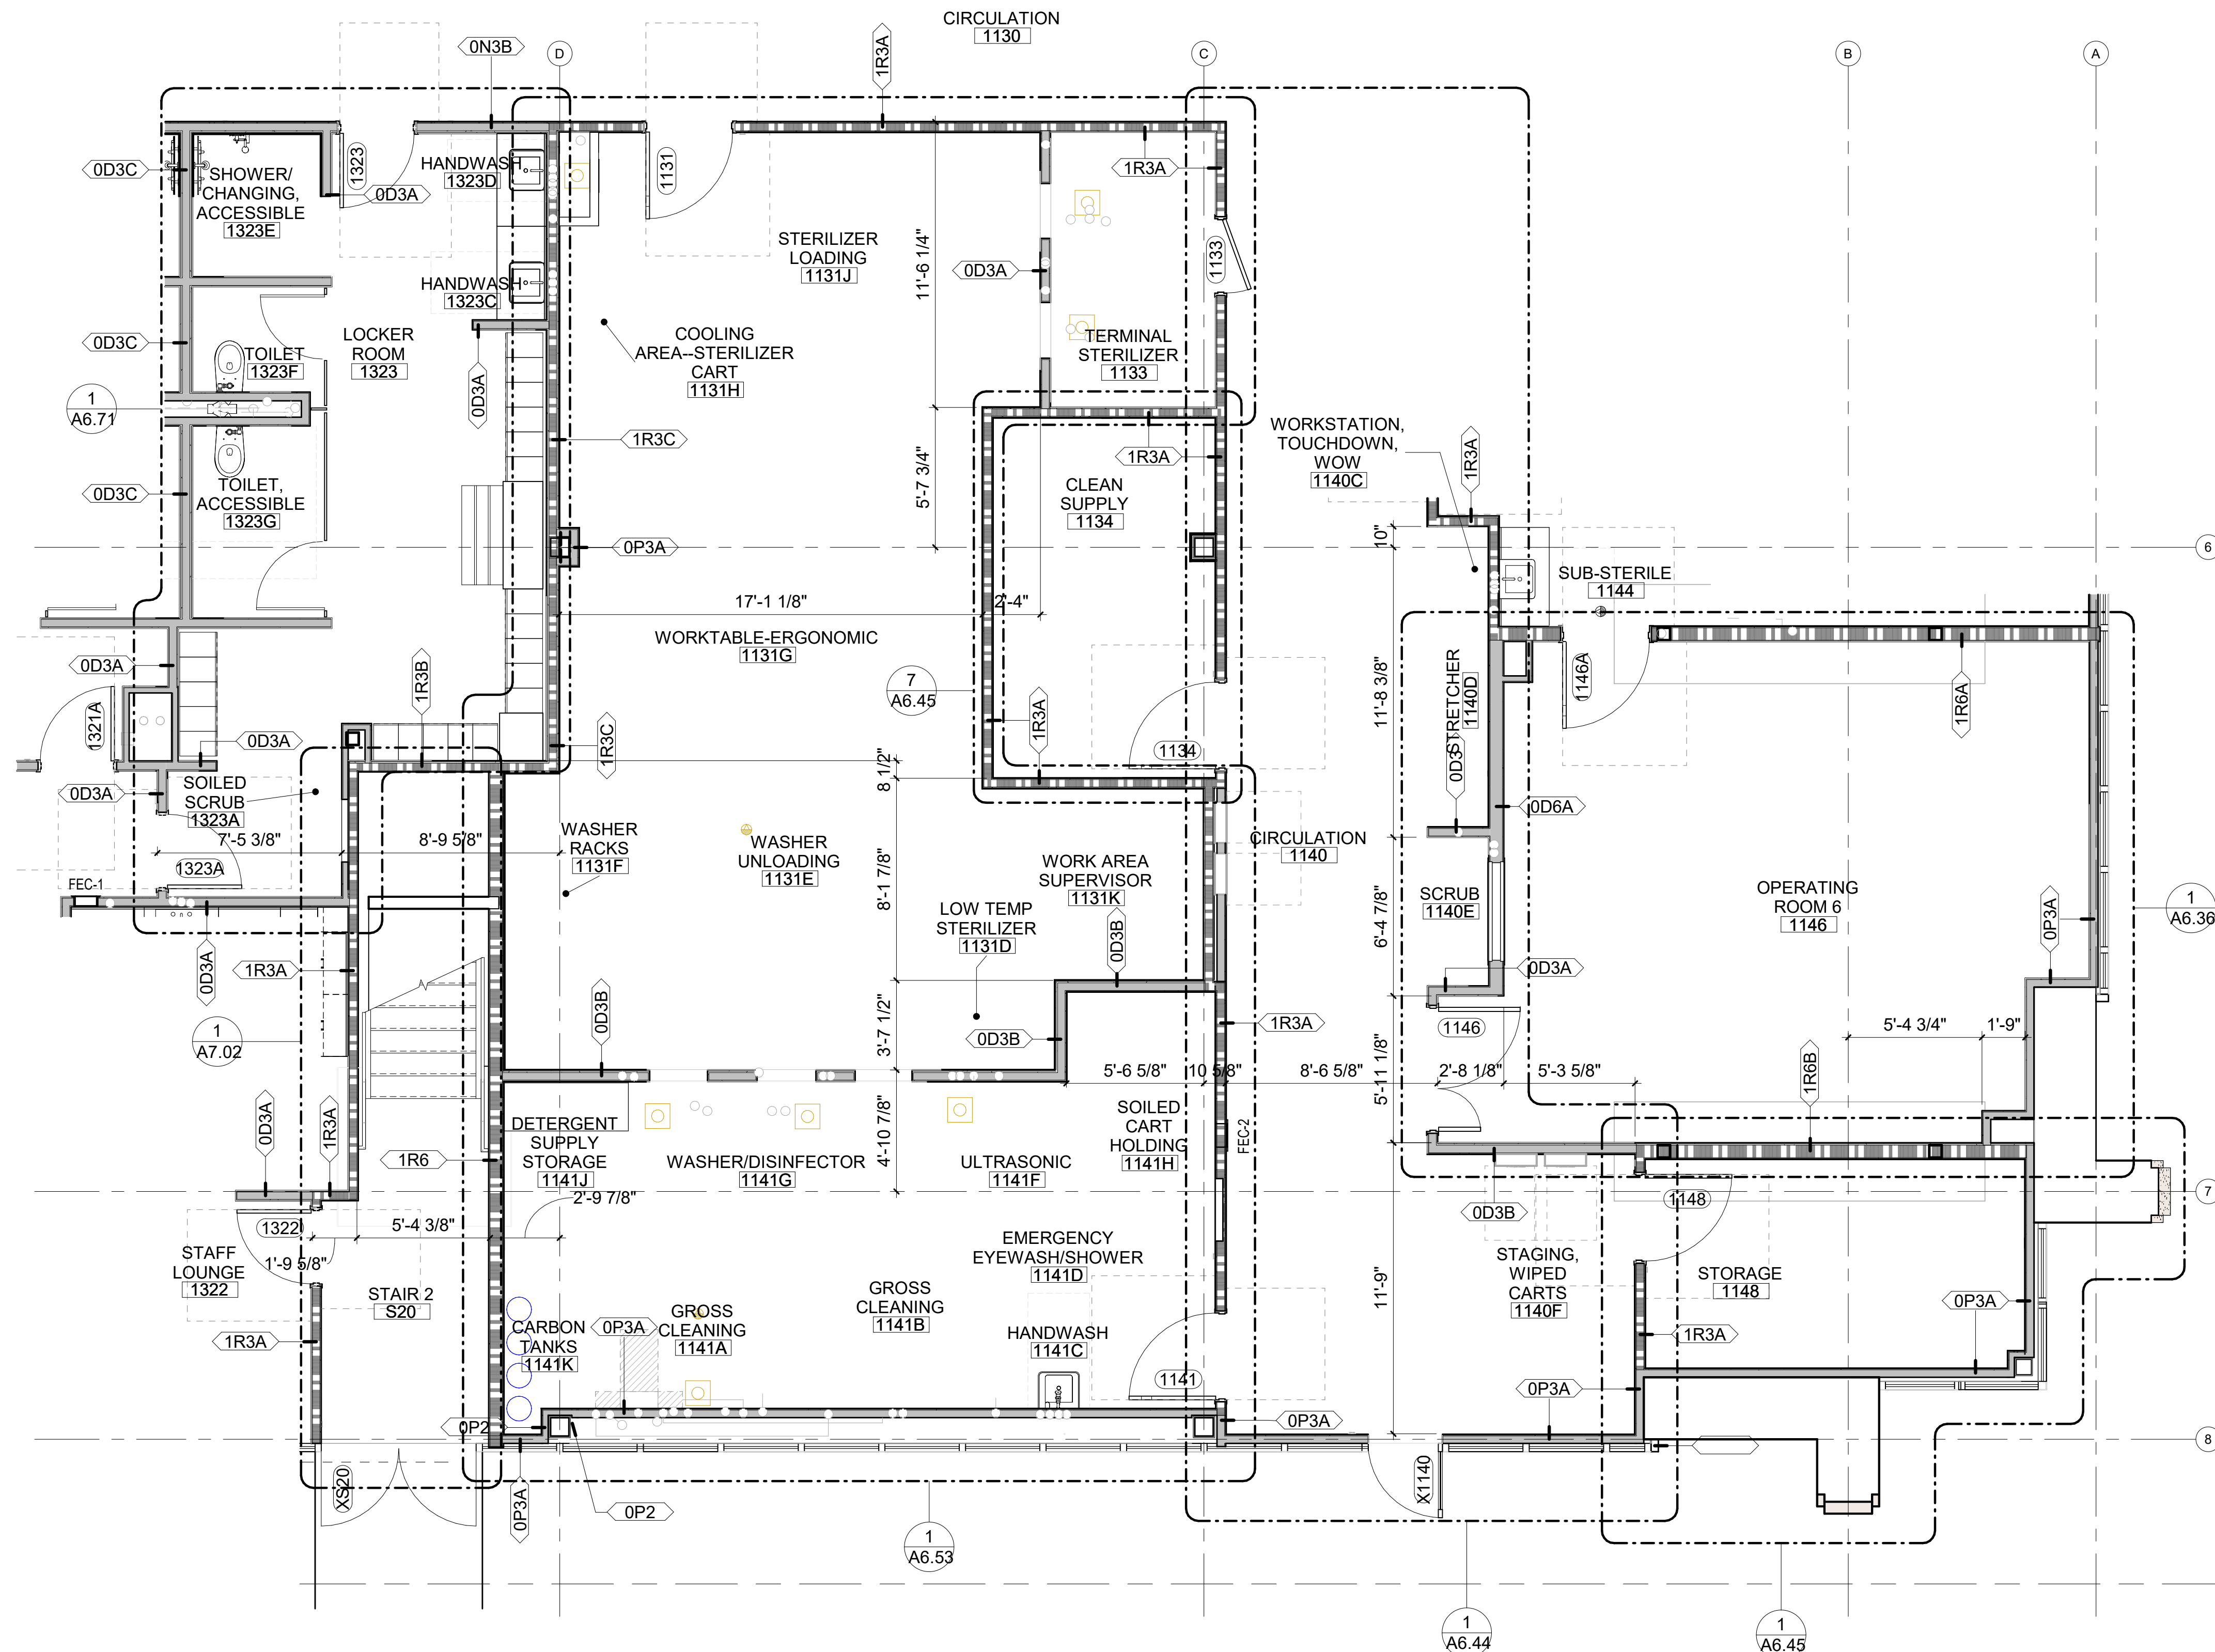

1 ENLARGED FLOOR PLAN LEVEL 1 - AREA F
1/4" = 1'-0"

GENERAL PLAN NOTES



1. CONTRACTOR TO NOTIFY ARCHITECT OF ANY DISCREPANCY BETWEEN (E) CONDITIONS AND DRAWINGS PRIOR TO PROCEEDING WITH CONSTRUCTION WORK.
2. SEE STRUCTURAL, TECHNOLOGY, MEP DWGS FOR EXTENT OF WORK.
3. SEE SHEET A1 SERIES, CIVIL & LANDSCAPE DWGS. FOR SITE PLAN AND THE EXTENT OF WORK AROUND THE BUILDING
4. SEE SIGNAGE SHEET SERIES SG FOR SIGNAGE INFORMATION
5. CONTRACTOR TO COORDINATE FIRE SPRINKLER AND FIRE ALARM SYSTEM.
6. EMERGENCY OUTLETS AND NURSE CALL SHOWN ON ELEC AND TECH DWGS
7. SEE G4.01, G4.02, G4.03, & G4.04 FOR TYP. MOUNTING HTS., PROVIDE BLOCKING FOR ALL WALL MOUNTED ITEMS PER DETAILS
8. SEE SHEET A2.31, A2.32, A9.05 FOR FINISHES AND A9.06 FOR TYP. RESTROOM ACCESSORIES. SEE A2.33 FOR FURNITURE
9. SEE A4.01 SERIES AND A4.02 FOR RCPS.
10. SEE A9.03A-C FOR EQPT. SCHDL AND A9.06 FOR IT EQPT SCHDL
11. ALL WALLS 0D3A U.O.N. ON A2.01A-A2.01F

KEYNOTES

#	NOTE
---	------

LEGEND

- NEW 1-HOUR RATED FIRE SMOKE BARRIER
NEW 1-HOUR RATED FIRE BARRIER
EXISTING PARTITION TO REMAIN
NEW UNRATED PARTITION
CUT AND PATCH (E) TPO ROOF

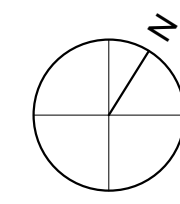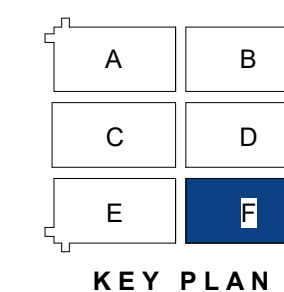

1420 SUTTER ST
SAN FRANCISCO, CA 94109
T 415.391.7918 F 415.391.7309
TEFarch.com



CONSULTANTS:
STRUCTURAL: FORELL|ELSESSER
CIVIL: SANDIS
LANDSCAPE: CREO
LOW VOLTAGE: INTROBA
ACOUSTICAL: SALTER
CODE: JENSEN HUGHES

SHC Hacienda
Lakes Ambulatory
Surgical Center

4457 Willow Rd
Pleasanton, CA



Project Number	22235.00	Issue Date	12/19/2025
Scale	As indicated	Phase	CD
Print Date	12/18/2025 3:05:29 PM		
No.	Date	Description	
1	12/19/2025	PERMIT SET	

ENLARGED LEVEL 1
FLOOR PLAN - AREA
F

A2.01F



1420 SUTTER ST
SAN FRANCISCO, CA 94109
T 415.391.7918 F 415.391.7309
TEFarch.com



Health Care

CONSULTANTS:
STRUCTURAL: FORELL|ELSESSER
CIVIL: SANDIS
LANDSCAPE: CREO
LOW VOLTAGE: INTROBA
ACOUSTICAL: SALTER
CODE: JENSEN HUGHES

SHC Hacienda Lakes Ambulatory Surgical Center

4457 Willow Rd
Pleasanton, CA



Project Number: 22235.00 Issue Date: 12/19/2025

Scale: 1/8" = 1'-0" Phase: CD
Print Date: 12/18/2025 3:05:33 PM


No. Date Description
1 12/19/2025 PERMIT SET

OVERALL FLOOR PLAN - LEVEL 2

A2.02

GENERAL NOTES

- CONTRACTOR TO NOTIFY ARCHITECT OF ANY DISCREPANCY BETWEEN (E) CONDITIONS AND DRAWINGS PRIOR TO PROCEEDING WITH CONSTRUCTION WORK.
- SEE STRUCTURAL, TECHNOLOGY, MEP DWGS FOR EXTENT OF WORK.
- SEE SHEET A1 SERIES, CIVIL & LANDSCAPE DWGS. FOR SITE PLAN AND THE EXTENT OF WORK AROUND THE BUILDING
- SEE SIGNAGE SHEET SERIES SG FOR SIGNAGE INFORMATION
- CONTRACTOR TO COORDINATE FIRE SPRINKLER AND FIRE ALARM SYSTEM.
- EMERGENCY OUTLETS AND NURSE CALL SHOWN ON ELEC AND TECH DWGS
- SEE G4.01, G4.02, G4.03, & G4.04 FOR TYP. MOUNTING HTS., PROVIDE BLOCKING FOR ALL WALL MOUNTED ITEMS PER DETAILS
- SEE SHEET A2.31, A2.32, A9.05 FOR FINISHES AND A9.06 FOR TYP. RESTROOM ACCESSORIES. SEE A2.33 FOR FURNITURE
- SEE A4.01 SERIES AND A4.02 FOR RCPS.
- SEE A9.03A-C FOR EQPT. SCHDL AND A9.06 FOR IT EQPT SCHDL
- ALL WALLS 0D3A U.O.N. ON A2.01A-A2.01F

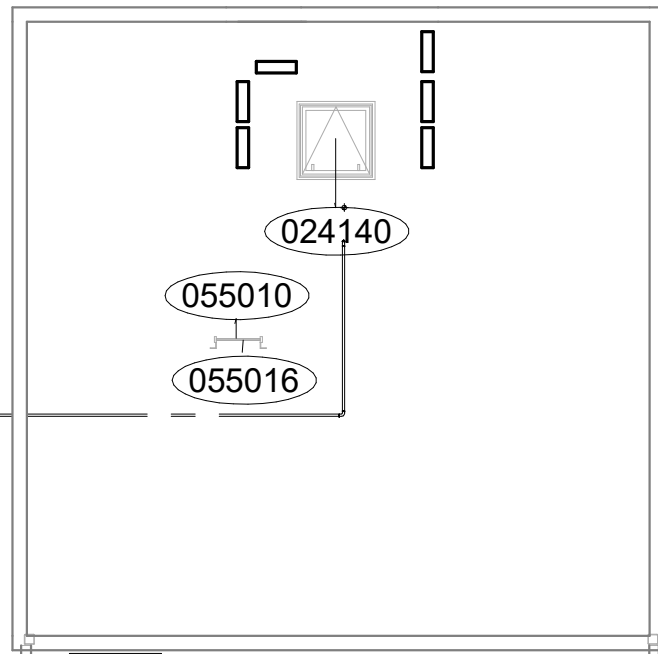

② LEVEL 2 - (E) MEZZANINE PLAN
1/8" = 1'-0"

KEYNOTES

#	NOTE
024140	PROTECT (E) ROOF HATCH
055010	(E) ROOF LADDER
055016	(E) ROOF LADDER TO REMAIN

LEGEND

- NEW 1-HOUR RATED FIRE-SMOKE BARRIER
- NEW 1-HOUR RATED FIRE BARRIER
- NEW UNRATED PARTITION
- EXISTING PARTITION TO REMAIN
- NEW INFILLED CONCRETE FILLED MTL DECK. SSD

